


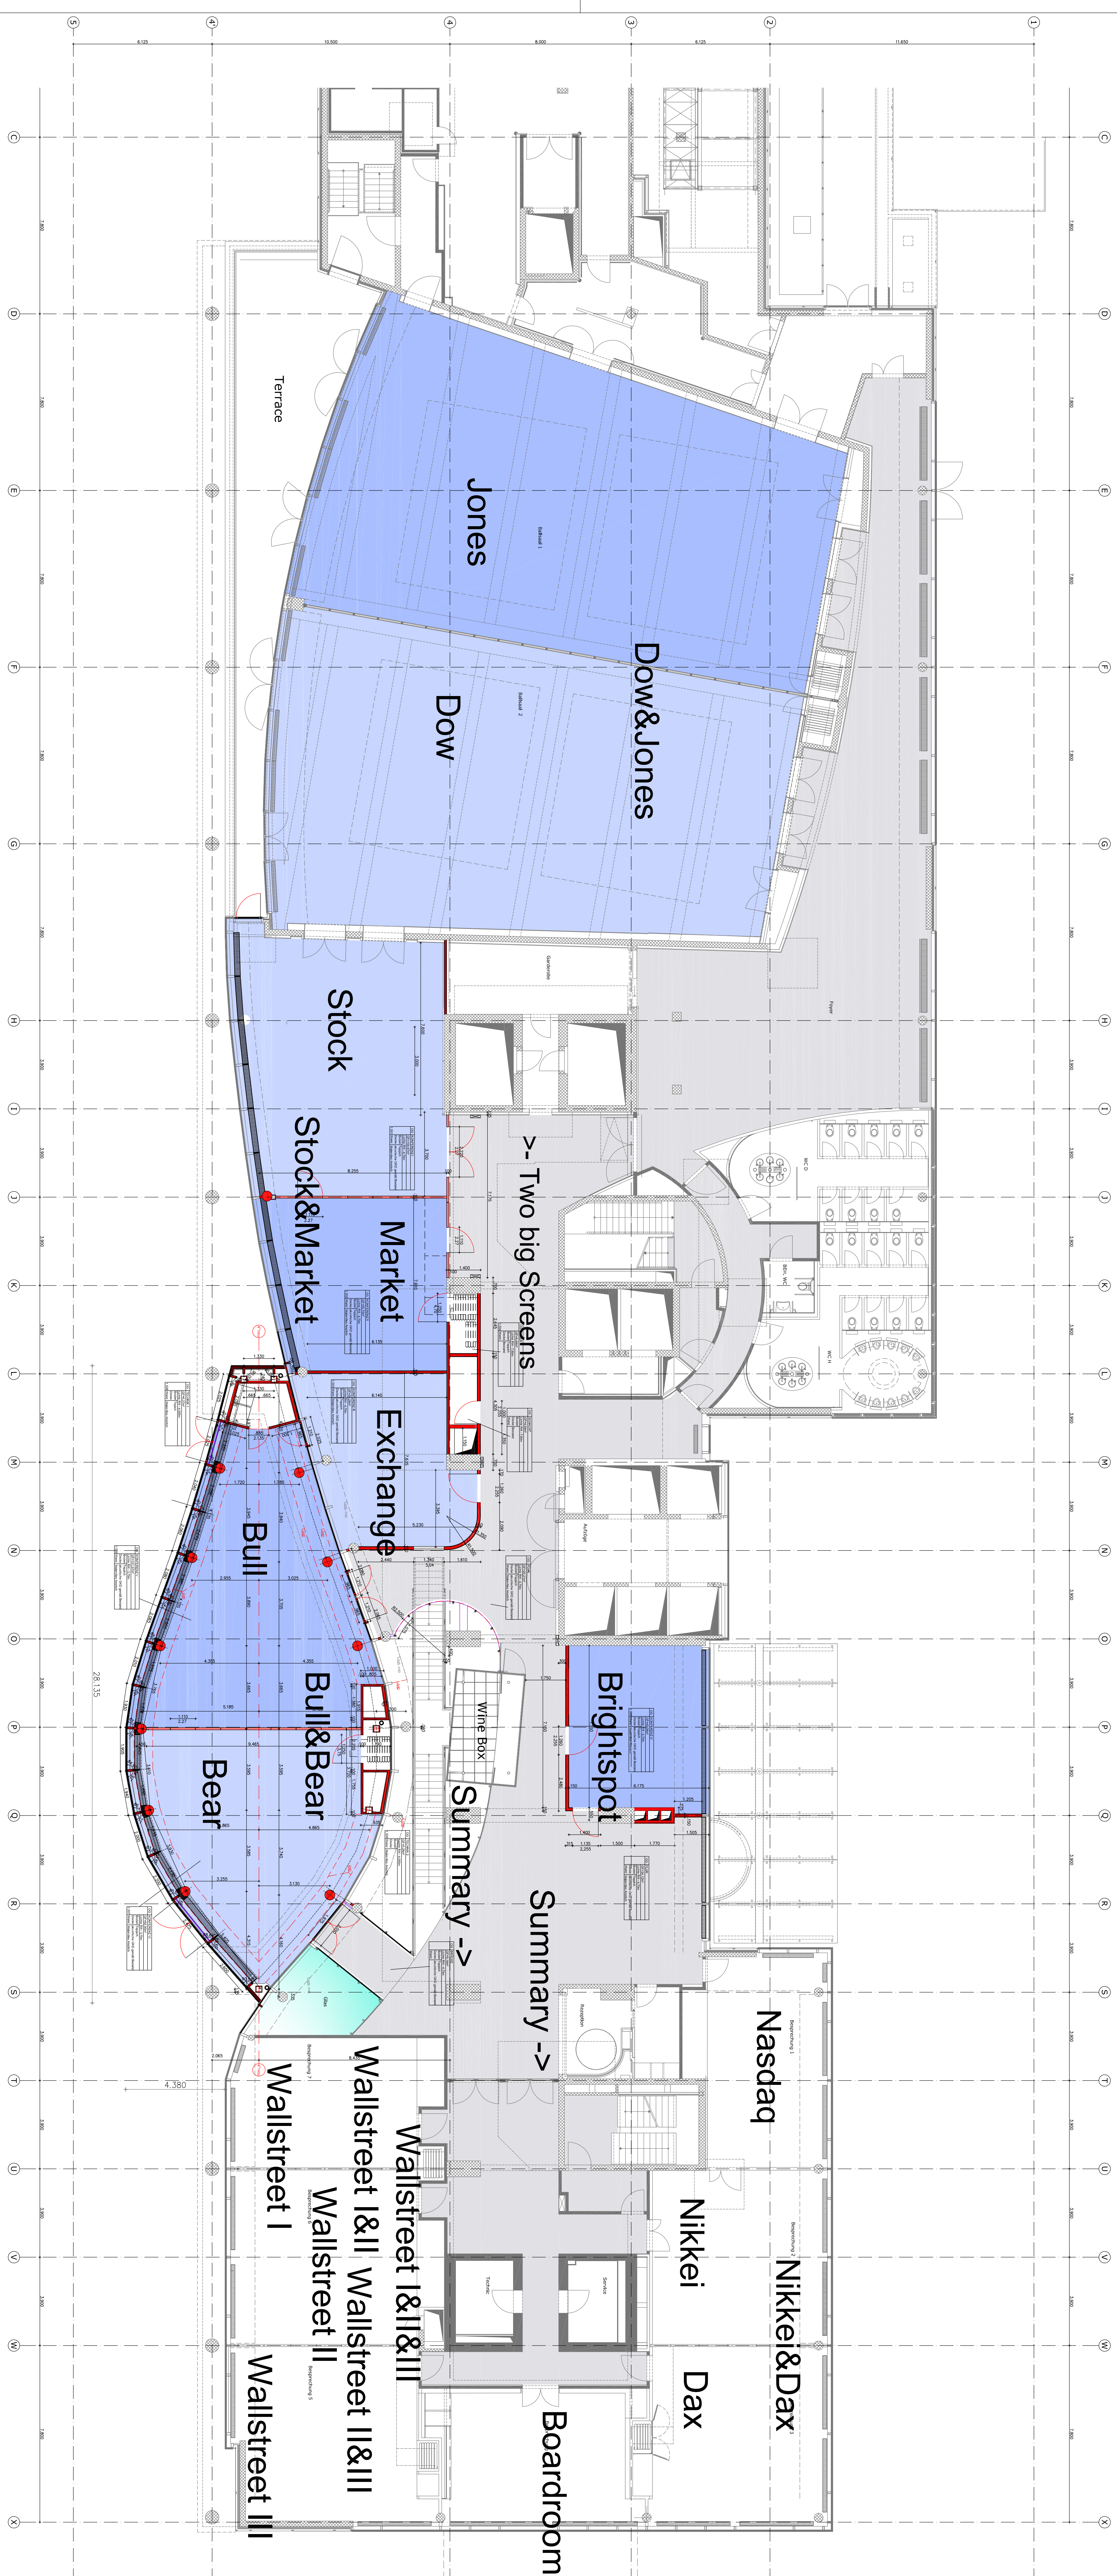

LEGENDE ERLÄUTERUNG

ALLE TÜRHOHEN VON OK-FIB
ALLE BRÜSTLENGEN VON OK-FIB
OK-FIB-LES = 1.003 (37,00 mm)

BEI UNMÄSSIGLICHEN VERKLEBENGEN

1:100	1m	2m	3m	4m	5m	6m
	1m	2m	3m	4m	5m	6m

1:50

0,5m	1m	1,5m
0,5m	1m	1,5m



1:25

ALLE MASSE SIND VOR AUSFÜHRUNG VON UNTERSCHNITTEN ZU PROFILIEREN
ALLE INNEN- UND AUßEN-RÄUME SIND ZU ENTWÄSSEN
ALLE MASSEN SIND ROLLMASSE

10		
09		
08		
07		
06		
05		
04		
03		
02		
01		
INDEX:	NAME: ABERBRUGEN	DATE:

WEITERGABE SOWIE VERNETZUNGSFÄHIGKEIT DIESER UNTERLAGE, VERKÄUFUNG UND MITTEILUNG IHRES INHALTS IST NICHT GESTÄTTET, SOWEIT NICHT AUSDRÜCKLICH ZUGESTANDEN. ZWISCHENVERHANDLUNGEN VERPFLICHTEN ZU SCHADENSERSATZ. ALLE RECHTE FÜR DEN FALL DER PATENTVERTEILUNG ODER GEBRAUCHSMUSTER-EINTRAGUNG VORBEHALTEN.

ÜBERSICHT MASSSTAB 1:100

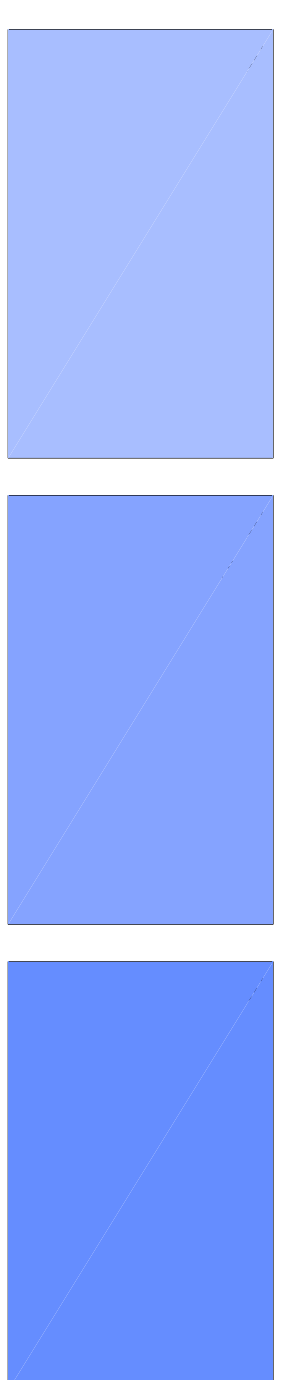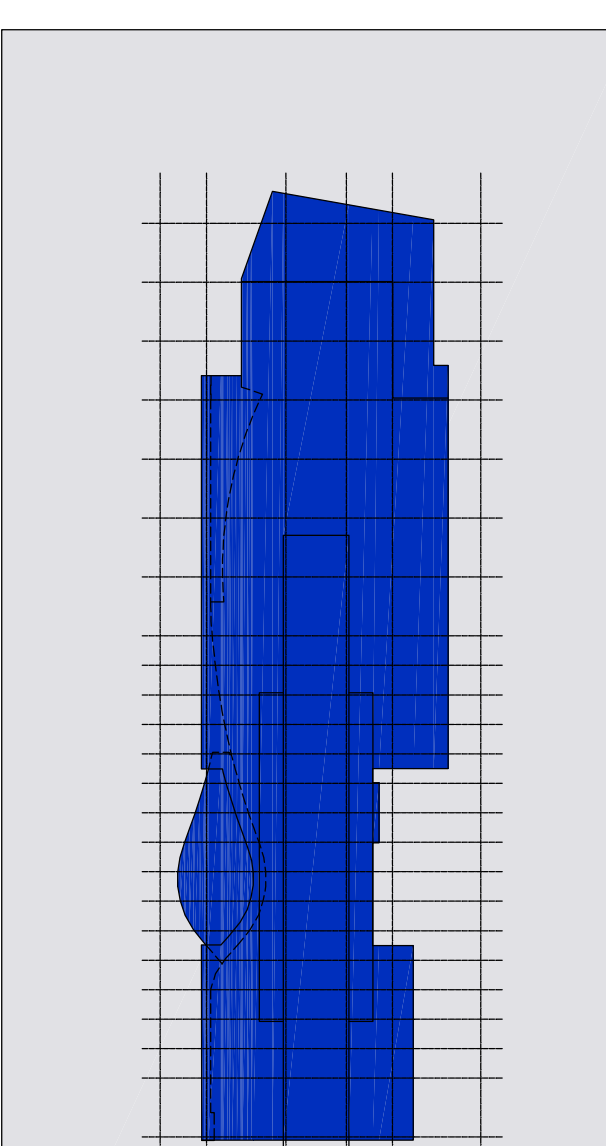

BAUSCHREIBEN: Tafelstellung der Decke über EG Eingangsbereich in den Achsen G-5/0-5. Errichtung eines 2-geschlossigen Anbaus und Teilklosgeschoss auf der Terrasse im EG Franklinstraße 65, 60486 Frankfurt am Main	
BALKEN: Franklinstrasse 65, Frankfurt am Main GmbH & Co. KG, Herrn Lars Weinans Am Ocker 7, 26550 Harlesene, Deutschland	DATUM: 28.01.2007 GRÜNDUNG: pt

PLANUNG:	ÜBERSICHT 1. OBERGESCHOSS	PROJEKTION: 1 / 100
PLANUNGSGESELLSCHAFT JACOBS	FORUM 80	13.1.2014

 **architekten + ingenieure + sachverständige**

- **Bahnstrasse 15 • 61462 Königstein**
- **fon 06174.6390.0 • fax 06174.6390.50**
- **info@jacobs-architekten.de • www.jacobs-architekten.de**

INDEX

00